


- In-situ seabed
- Water
- Toe rock, Dn50 = 0.27 m
- Blinding layer
- Granular backfill
- Reinforced concrete

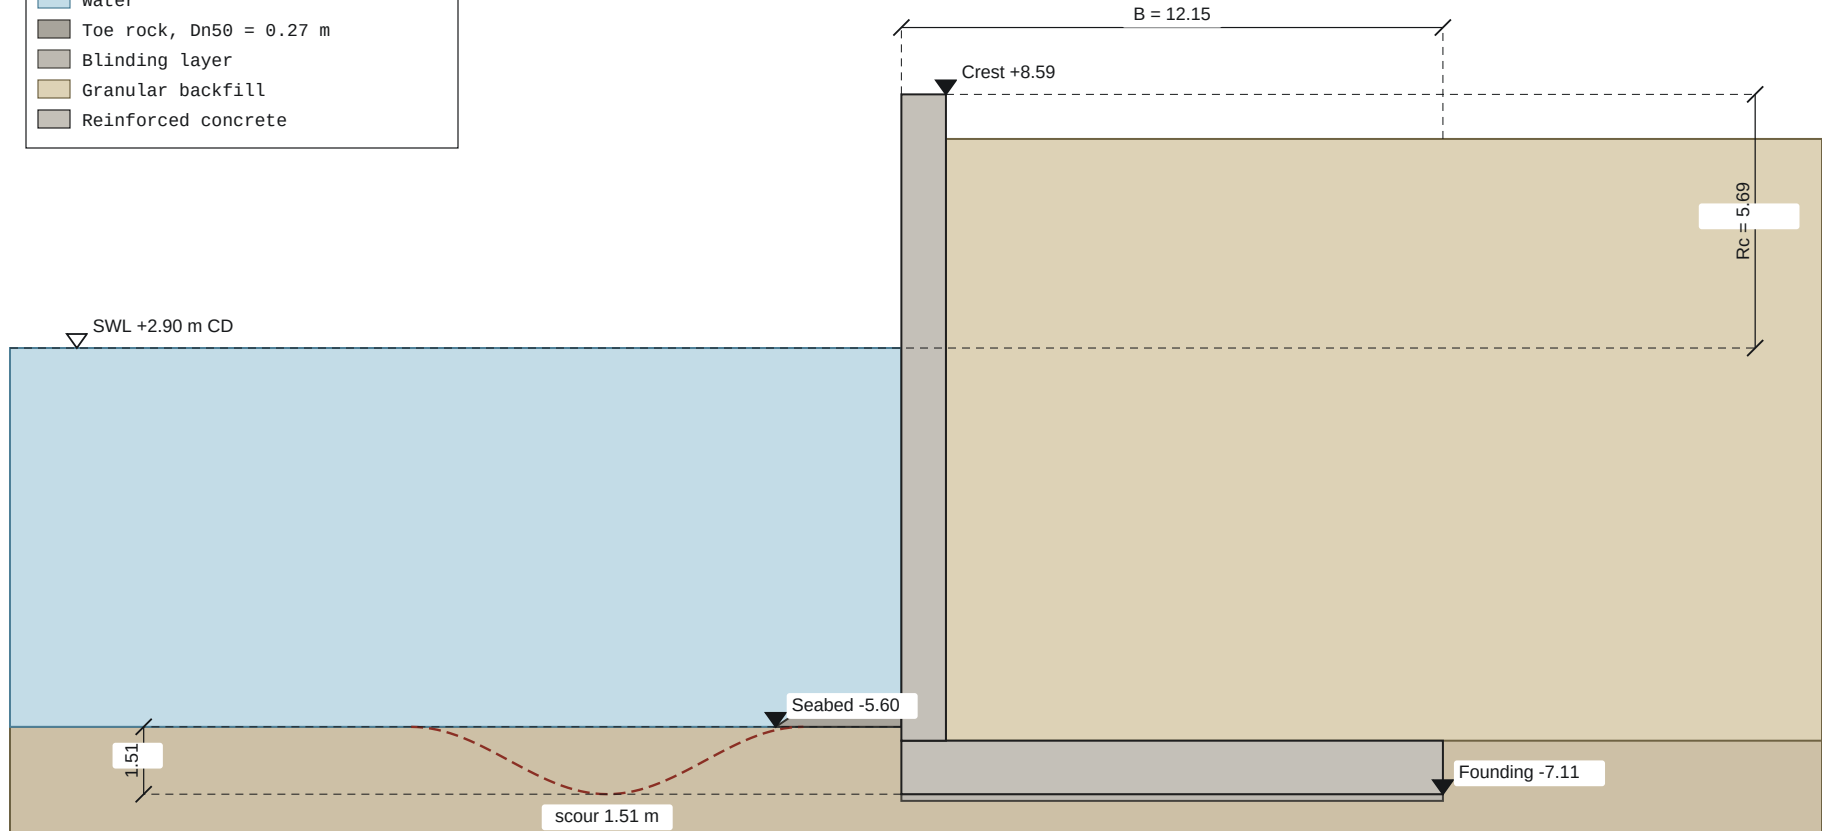

(A) SEAWALL TYPICAL SECTION
1:170 on screen

