


- In-situ seabed
- Water
- Bedding blanket, coarse sand, 1.25 m
- Quarry run core
- Filter layer, Dn50 = 0.83 m
- Armour, Dn50 = 1.80 m (15.4 t)
- Toe berm, Dn50 = 0.83 m (1.5 t), both toes
- Crown block, mass concrete
- Sand and gravel infill

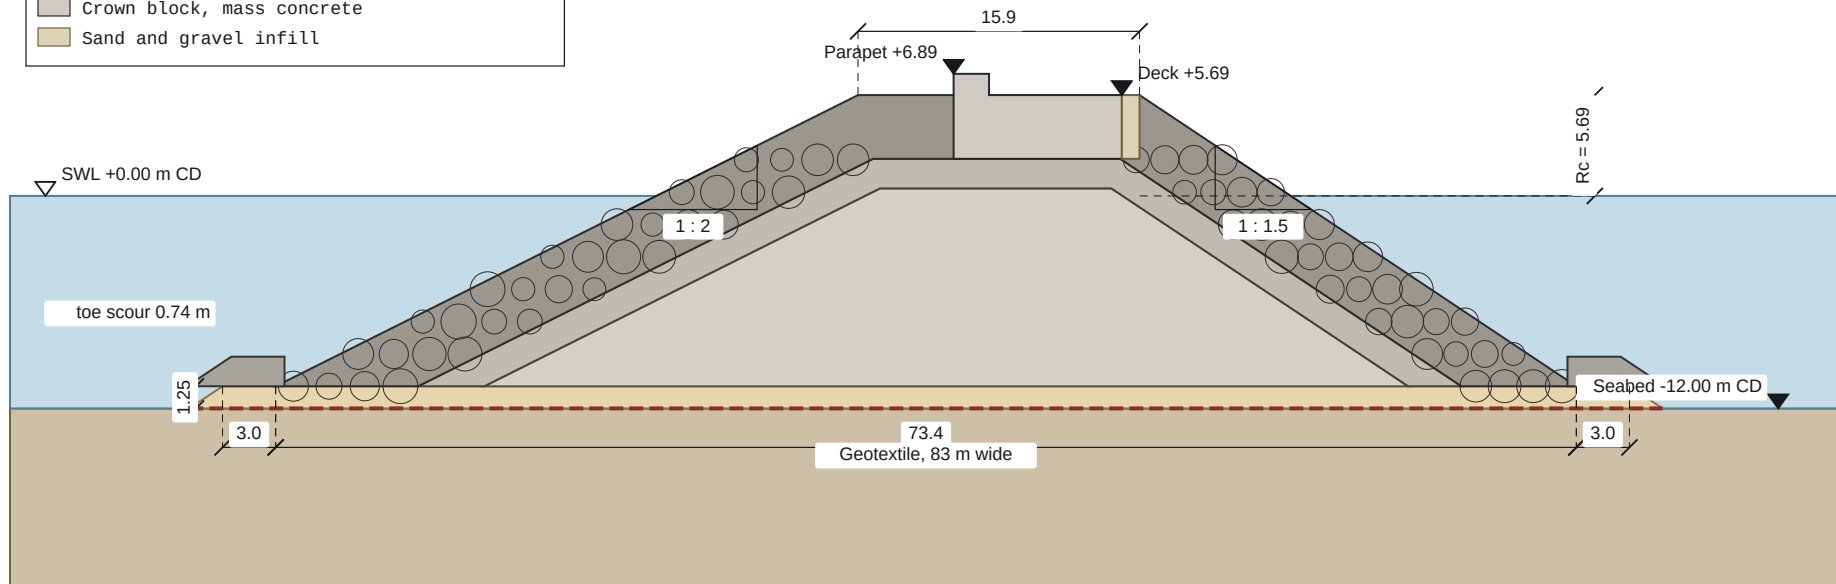

A

BREAKWATER TYPICAL SECTION

1:425 on screen

