


- In-situ seabed
- Water
- Bedding blanket, coarse sand, 1.16 m
- Quarry run core
- Filter layer, Dn50 = 0.78 m
- Armour, Dn50 = 1.67 m (12.3 t)
- Toe berm, Dn50 = 0.78 m (1.2 t), both toes
- Crown block, mass concrete
- Sand and gravel infill

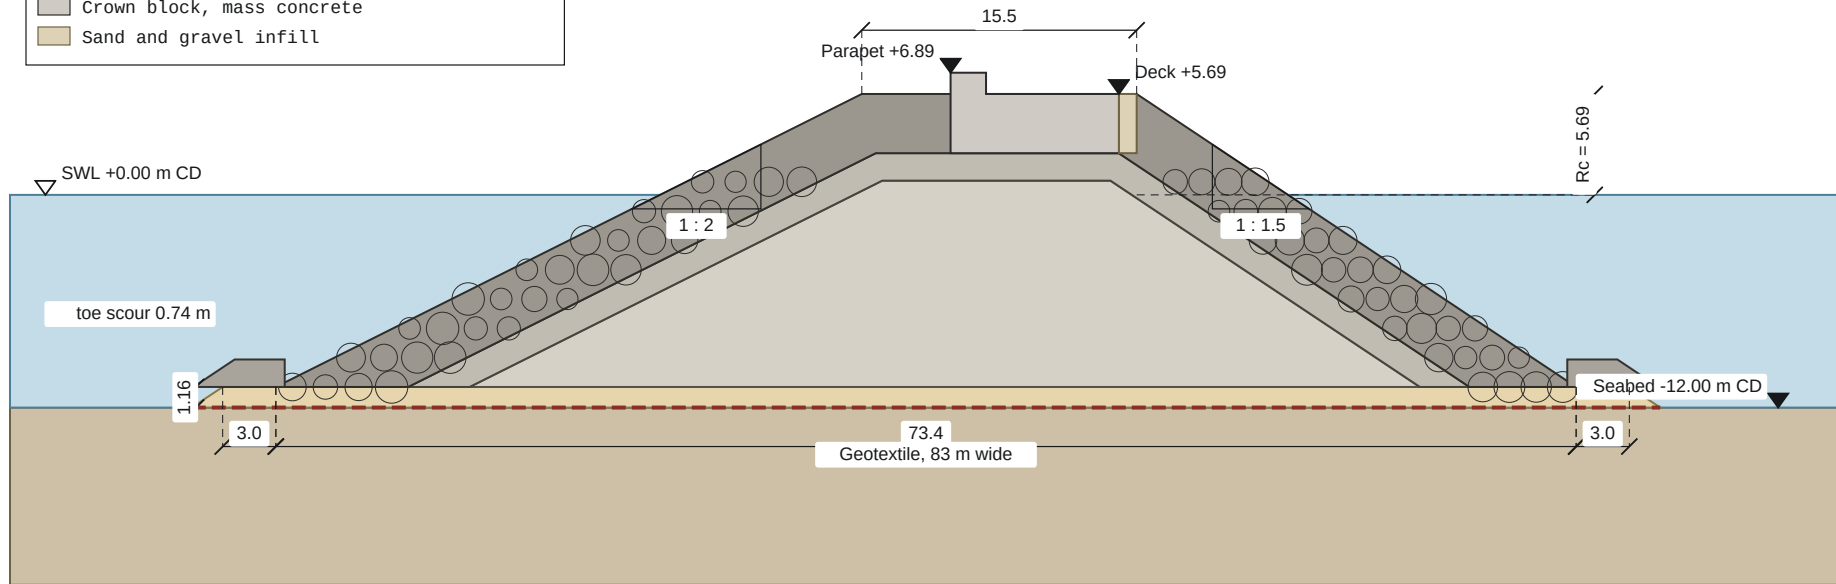

A

BREAKWATER TYPICAL SECTION

1:425 on screen

