


- In-situ seabed
- Water
- Toe rock, Dn50 = 0.31 m
- Blinding layer
- Granular backfill
- Reinforced concrete

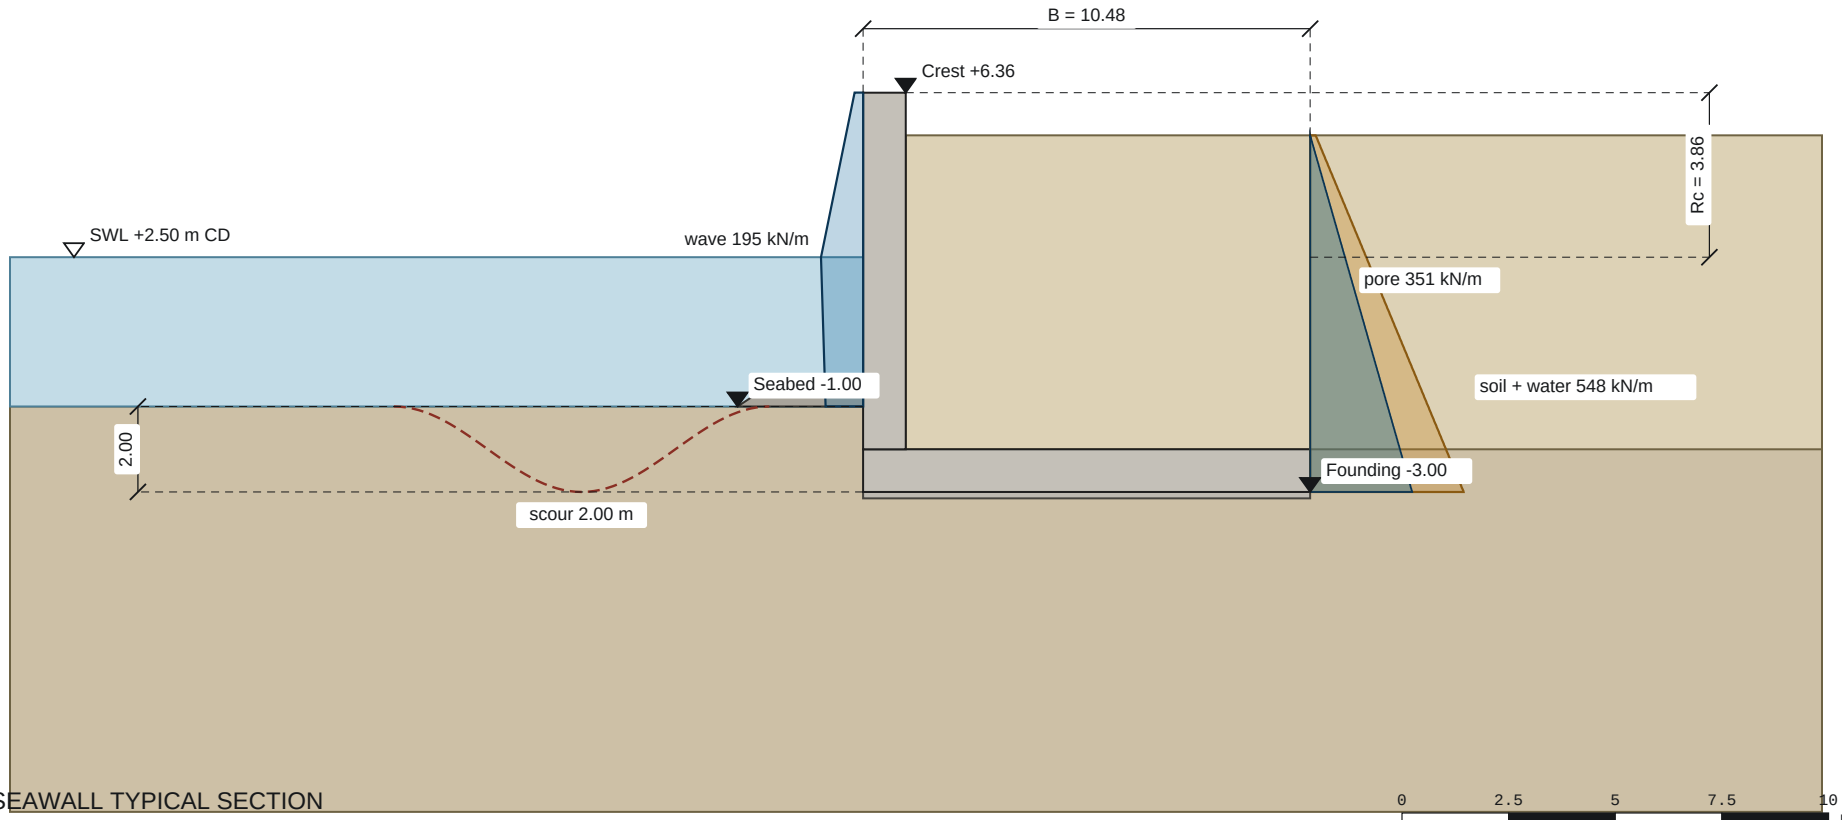

**SEAWALL TYPICAL SECTION**  
1:175 on screen governed by the drawdown

